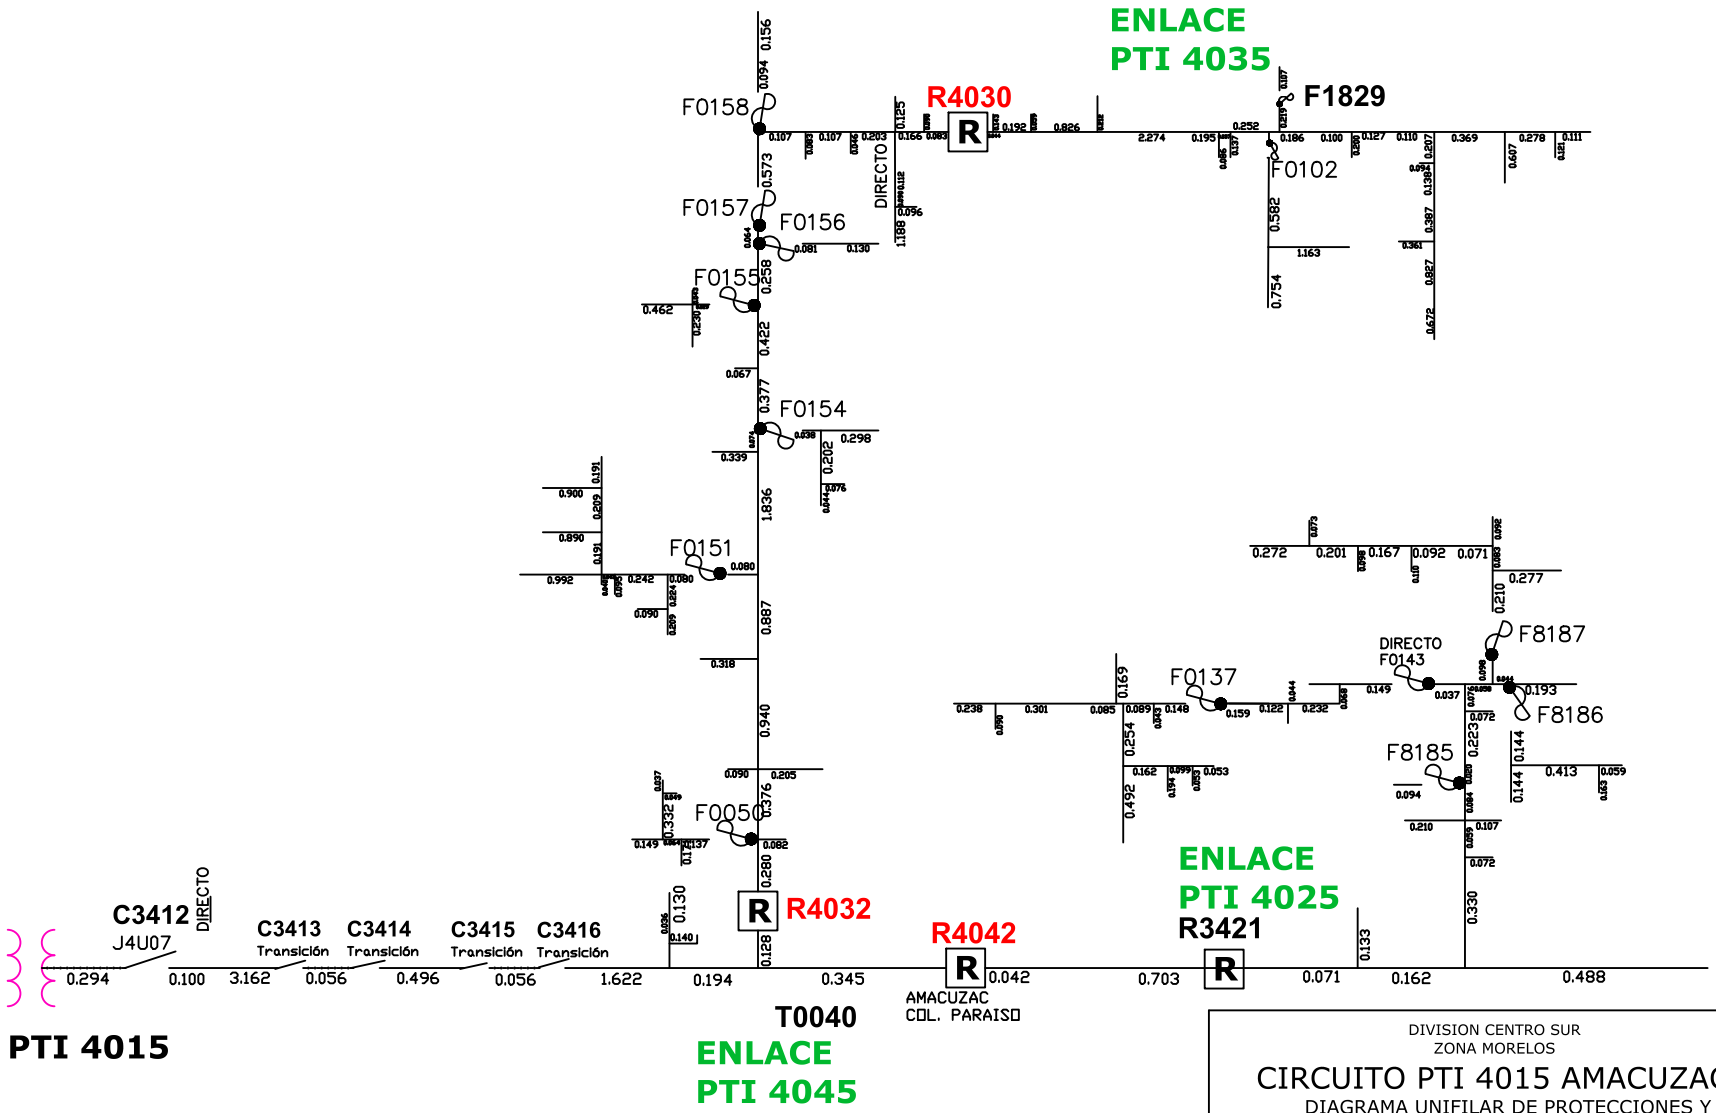

SUBESTACION	CIRCUITO	DEMANDA KW			NUMERO CLIENTES	POBLACIONES IMPORTANTES	SERVICIOS IMPORTANTES
		MAXIMA	MEDIA	MINIMA			
PUENTE DE IXTLA	4015	7,380	5,990	4,360	2,376	COLONIAS CENTRO, EL PARAISO, LOS ANGELES	BOMBAS DE AGUA POTABLE Y RIEGO, AMACUZAC

DIVISION CENTRO SUR
ZONA MORELOS

CIRCUITO PTI 4015 AMACUZAC

DIAGRAMA UNIFILAR DE PROTECCIONES Y SECCIONAMIENTOS

COMISION FEDERAL DE ELECTRICIDAD

ESCALA: S / E
PROYECTO: ING. G.C.B
DIBUJO: ING. S.S.R.E
SUPERVISO: ING. H.B.Z.

APROBO:
ING. ULISES CARMONA ONOFRE
SUPDTE. GRAL. ZONA MORELOS

FECHA: NOV. 2025
PROYECTO