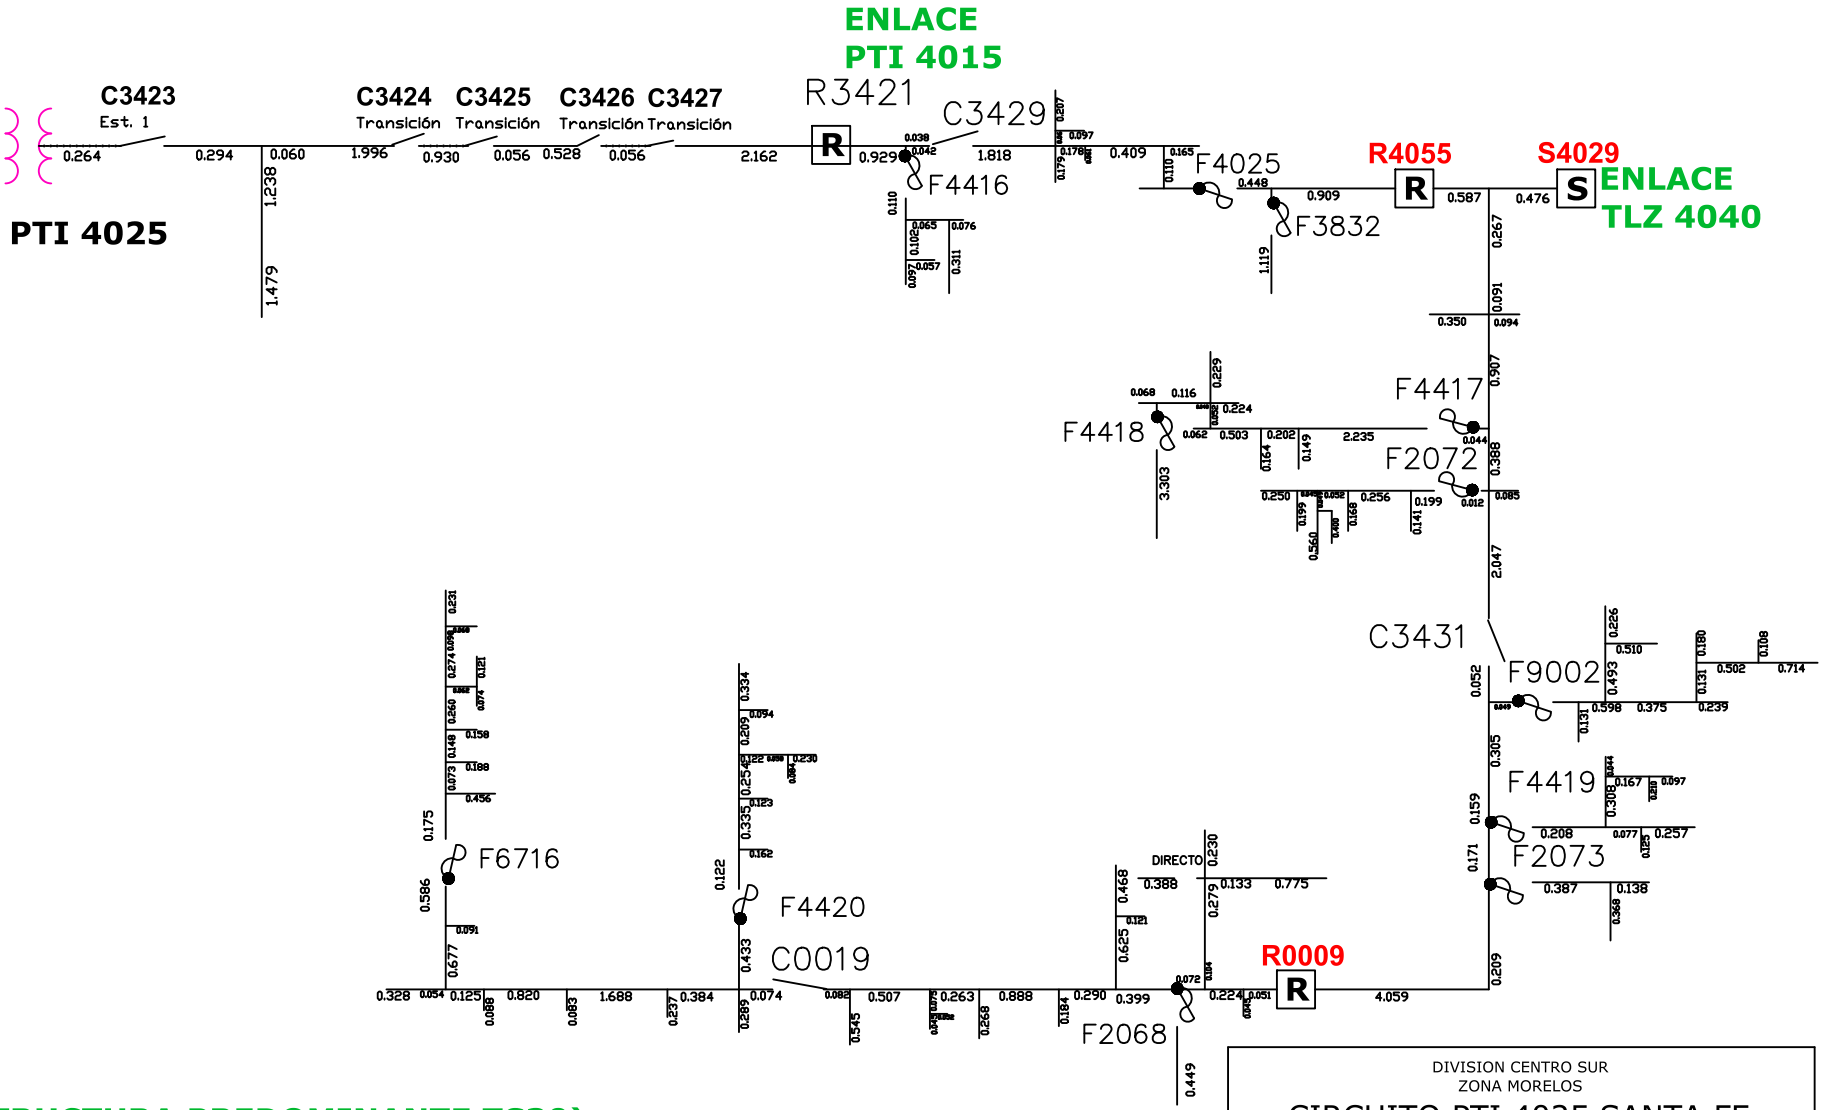

(ESTRUCTURA PREDOMINANTE TS30)

SUBESTACION	CIRCUITO	DEMANDA KW			NUMERO CLIENTES	POBLACIONES IMPORTANTES	SERVICIOS IMPORTANTES
		MAXIMA	MEDIA	MINIMA			
PUENTE DE IXTLA	4025	1,162	768	547	4,582	COAHUIXTLA, ZOQUITAL, CASAHUATLAN, PALMILLAS, ZACAPALCO, SANTA FE TEPETLAPA,	BOMBAS DE AGUA POTABLE Y RIEGO, CAPUFE

DIVISION CENTRO SUR
ZONA MORELOS

CIRCUITO PTI 4025 SANTA FE

DIAGRAMA UNIFILAR DE PROTECCIONES Y SECCIONAMIENTOS

COMISION FEDERAL DE ELECTRICIDAD

ESCALA: S / E	APROBO:	FECHA: NOV 2025
PROYECTO: ING. G.C.B DIBUJO: ING. S.S.R.E SUPERVISO: ING. H.B.Z	ING. ULISES CARMONA ONOFRE SUPDTE. GRAL. ZONA MORELOS	PROYECTO