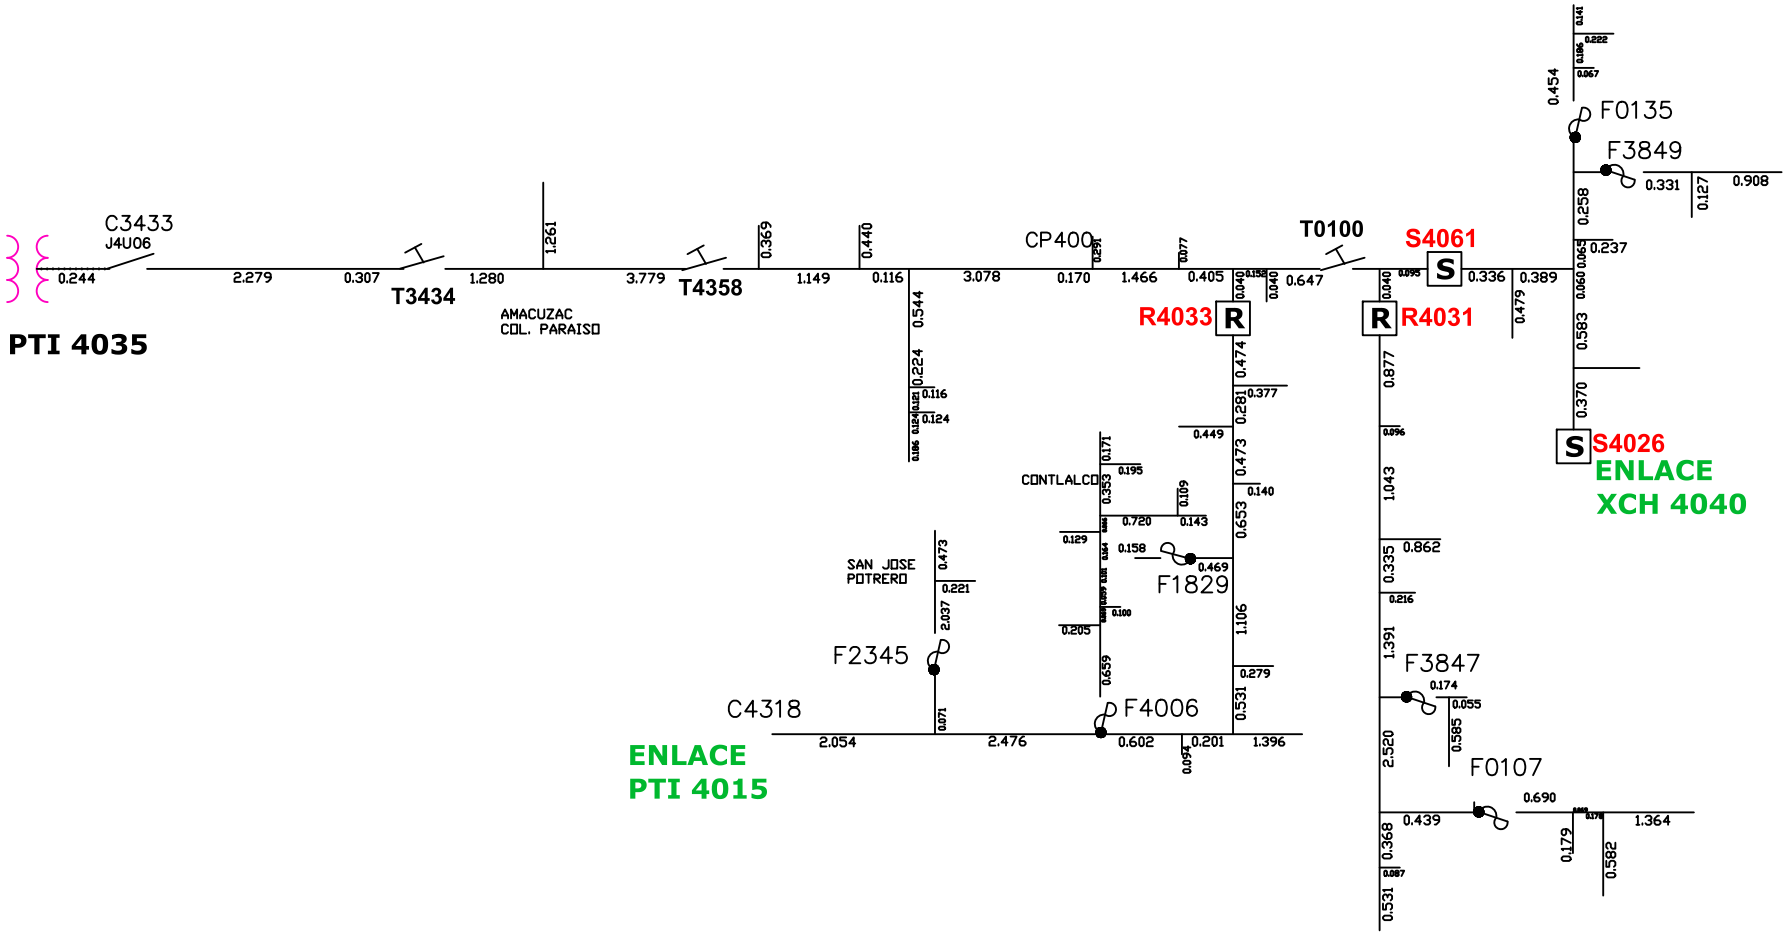

(ESTRUCTURA PREDOMINANTE TS30)

SUBESTACION	CIRCUITO	DEMANDA KW			NUMERO CLIENTES	POBLACIONES IMPORTANTES	SERVICIOS IMPORTANTES
		MAXIMA	MEDIA	MINIMA			
PUENTE DE IXTLA	4035	1,085	805	401	1,542	SAN JOSE POTRERO, CONTLALCO, MICHAPA, CACAHUAMILPA	GRUTAS DE CACAHUAMILPA, CEFERESO FEMENIL MICHAPA

DIVISION CENTRO SUR
ZONA MORELOS

CIRCUITO PTI 4035 MICHAPA

DIAGRAMA UNIFILAR DE PROTECCIONES Y SECCIONAMIENTOS

COMISION FEDERAL DE ELECTRICIDAD

ESCALA: S / E	APROBO:	FECHA: NOV. 2025
PROYECTO: ING. G.C.B DIBUJO: ING. S.S.R.E SUPERVISO: ING. H.B.Z.	ING. ULISES CARMONA ONOFRE SUPDTE. GRAL. ZONA MORELOS	PROYECTO